


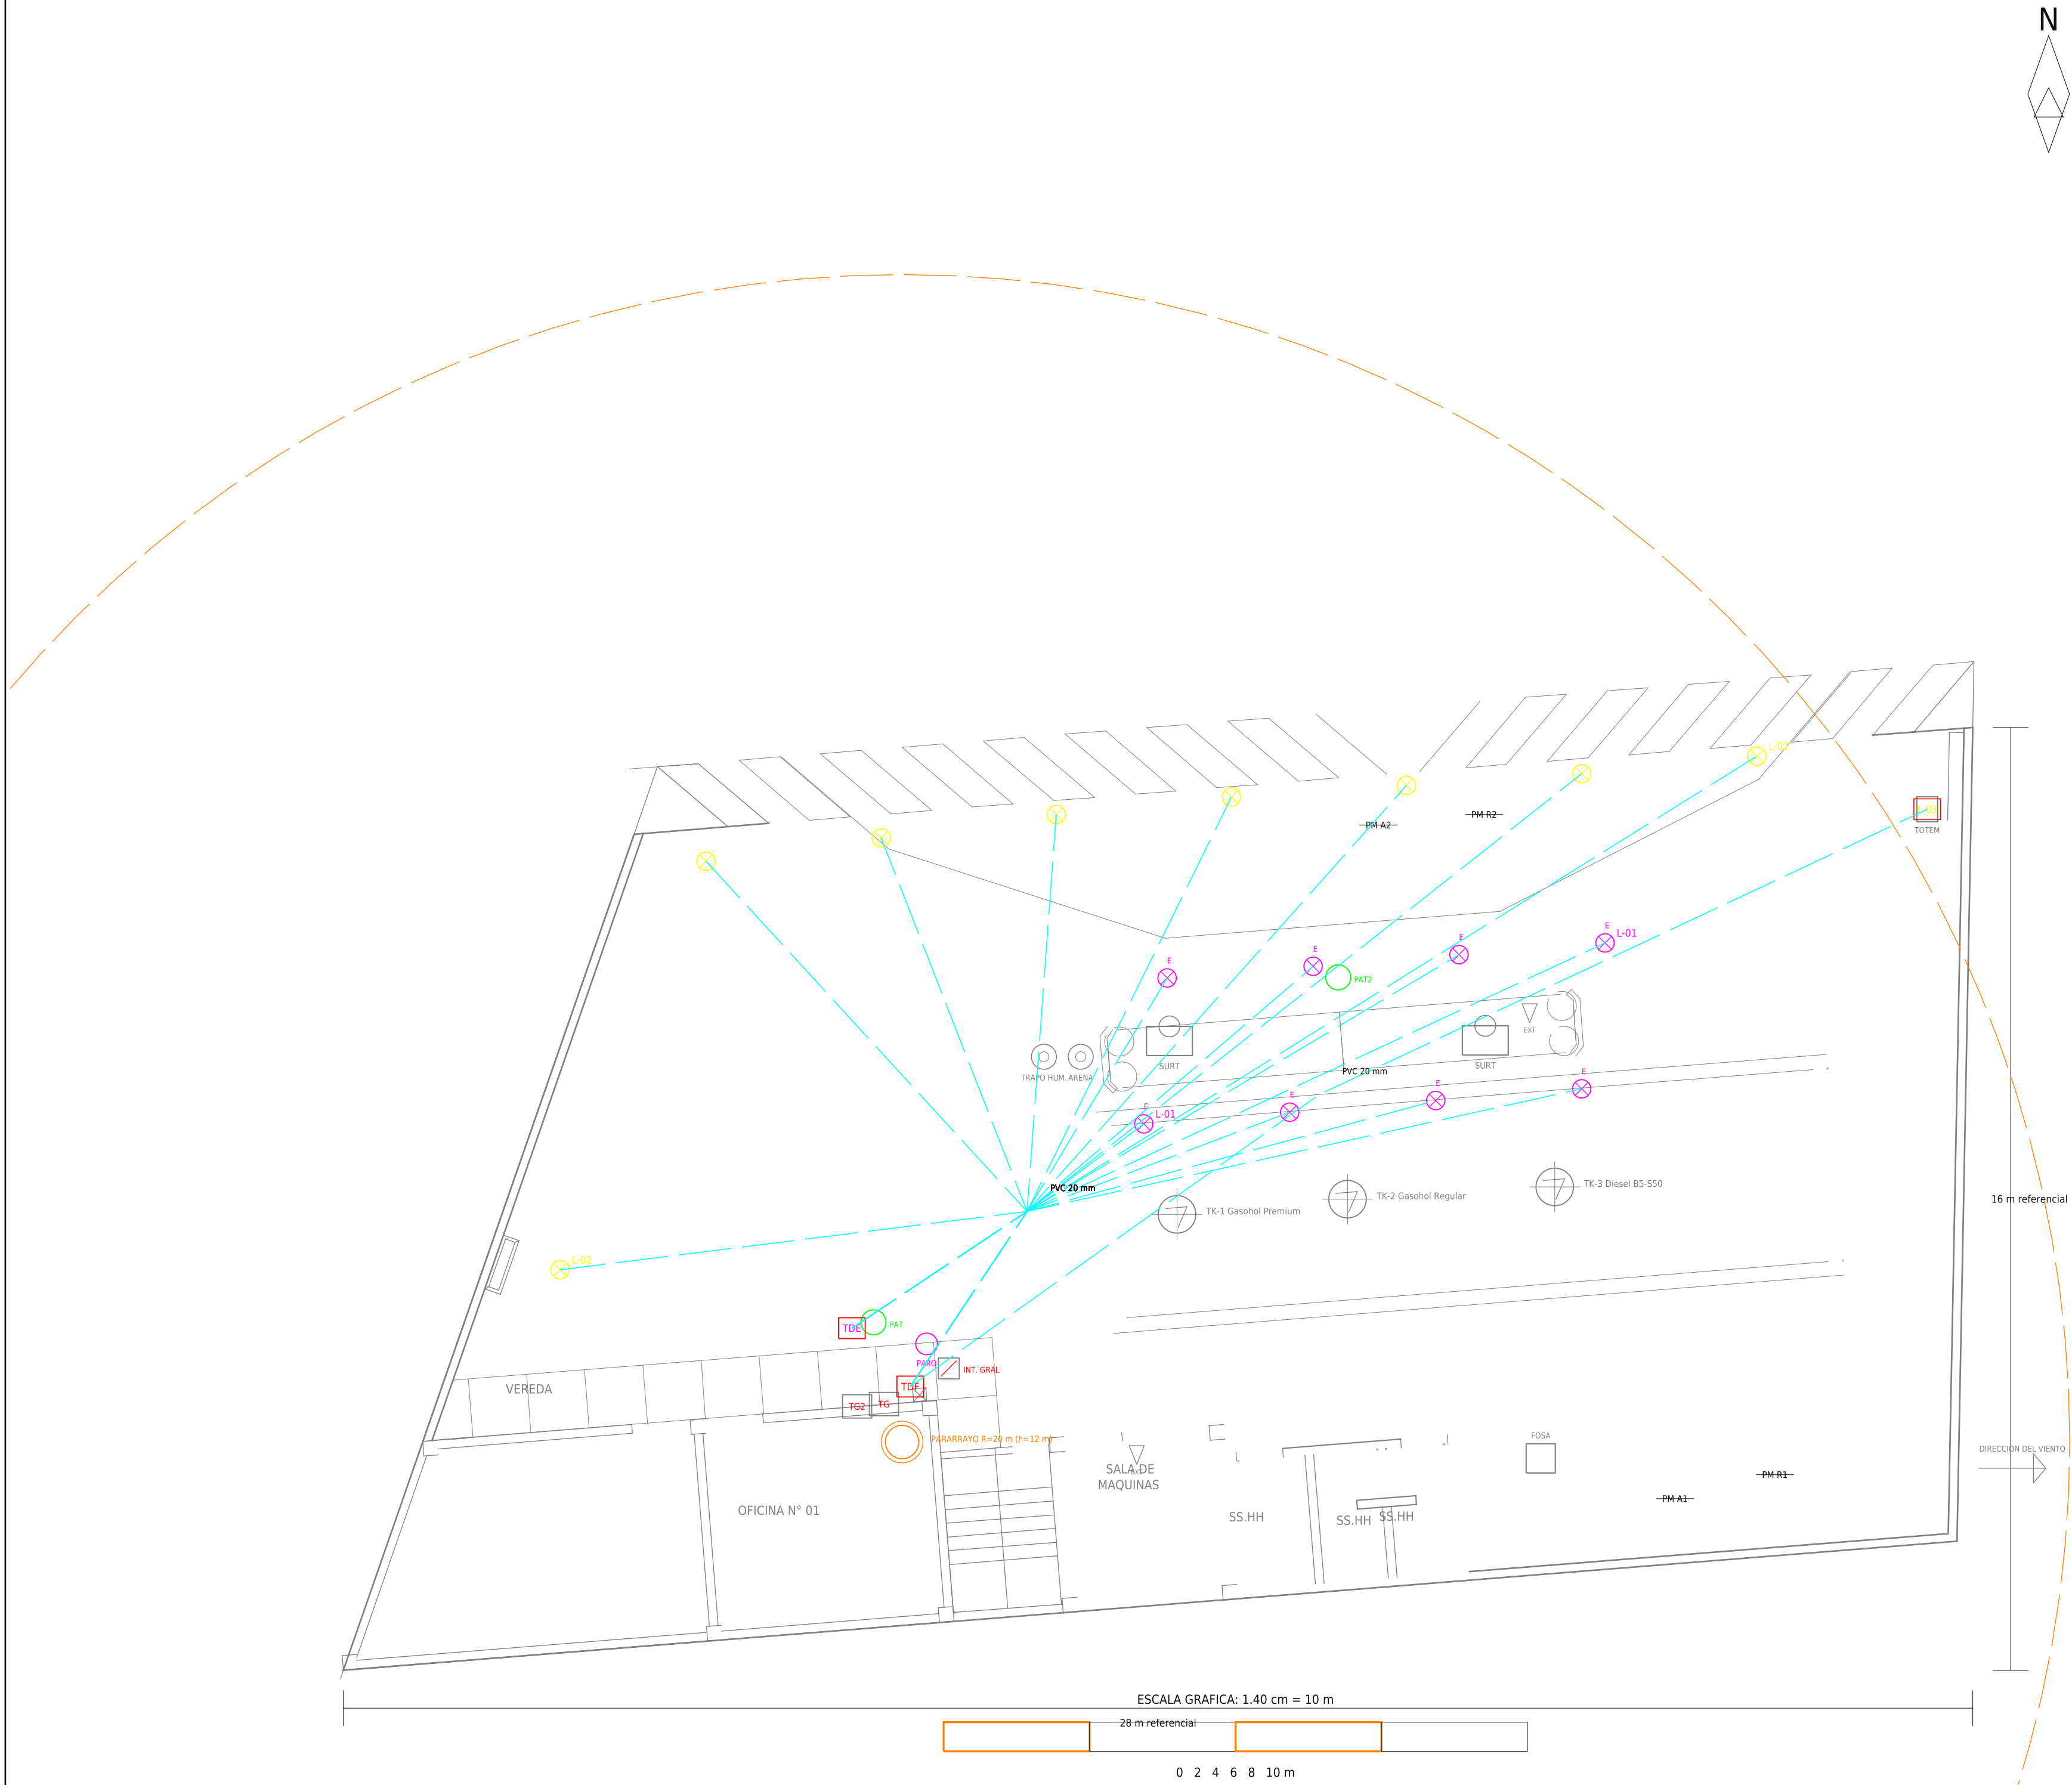

IE-01 LEYENDA Y CRITERIOS	
	Luminaria LED - circuito de emergencia (L-01, marquesina/despacho)
	Luminaria LED - alumbrado exterior normal (L-02, postes de patio)
	Tablero de distribucion TDE / TDF
	Tablero general TG / TG2 (observados en el DWG)
	Interruptor general de la instalacion
	Pulsador de paro de emergencia de playa
	Surtidor de doble manguera con cabeza electronica
	Tanque subterraneo TK con bomba sumergible (STP)
	Pozo de puesta a tierra (PAT / PAT2)
	Pararrayo R=20 m (h=12 m); circulo punteado = radio
	Punto de monitoreo de aire/ruido (PM A1/R1/A2/R2)
	Cilindros de seguridad (arena / trapo humedo)
	Fosa de agua
	Extintor
	Totem de precios / letrero (L-03)
	Direccion del viento
	Canalizacion subterranea proyectada
CNE: dV ramal <= 2.5 % y total <= 4 %; PE en todo circuito	

NOTAS TECNICAS
Tension: 380/220 V, 60 Hz, 3F+N+PE (sistema TN-S). Canalizaciones subterraneeas enterradas a 0.60 m bajo nivel de piso. Tuberia PVC SAP 20/25/32 mm segun calibre de conductores. Conductor de cobre XLPE, seccion minima 2.5 mm2. Toda luminaria de playa con proteccion IP66 y circuito de emergencia. Alimentadores a TDE/TDF con ITM 40/32 A y cable 10 mm2 (ver IE-05).

UNIVERSIDAD NACIONAL DEL ALTIPLANO				
FACULTAD DE INGENIERIA MECANICA ELECTRICA, ELECTRONICA Y SISTEMAS				
ESCUELA PROFESIONAL DE INGENIERIA MECANICA ELECTRICA				
PROYECTO: INSTALACIONES ELECTRICAS EN BAJA TENSION				
ESTACION DE SERVICIO (GRIFO) DE COMBUSTIBLES LIQUIDOS - ANTEPROYECTO NUEVO				
DIESEL B5-S50 / GASOHOL REGULAR / GASOHOL PREMIUM - SIN GLP NI GNV				
DISTRIBUCION GENERAL Y ALUMBRADO EXTERIOR				
PROPIETARIO: MIGUEL MAMANI CHUQUICALLATA DISTRITO/PROV.: SAN ROMAN - DEP.: PUNO UBICACION: PREDIO RUSTICO REUMITA PARCELA B-8 Y B-9, CARRETERA JULIACA-PUNO				
CURSO: INSTALACIONES ELECTRICAS I DOCENTE: MG. GREGORIO MEZA MAROCHO			DISENADO Y DIBUJADO: RENZO GABRIEL MAMANI GALINDO REVISION DOCENTE: CAMPO ACADEMICO - SIN FIRMA NI APROBACION AFIRMADA	
MODALIDAD: INDIVIDUAL CODIGO EST.: 228447			SEMESTRE: 2026-II SEDE: PUNO - PERU	
LAMINA IE-01	ESCALA 1:100 / IND.	FECHA AGOSTO 2026	REV. R00	HOJA 01/06
UNAP - PUNO ANTEPROYECTO SUJETO A VERIFICACION DE CAMPO, FACTIBILIDAD Y REVISION PROFESIONAL		NO SE CONSIGNA CIP, SELLO NI FIRMA POR NO EXISTIR ESOS DATOS EN LAS FUENTES		