


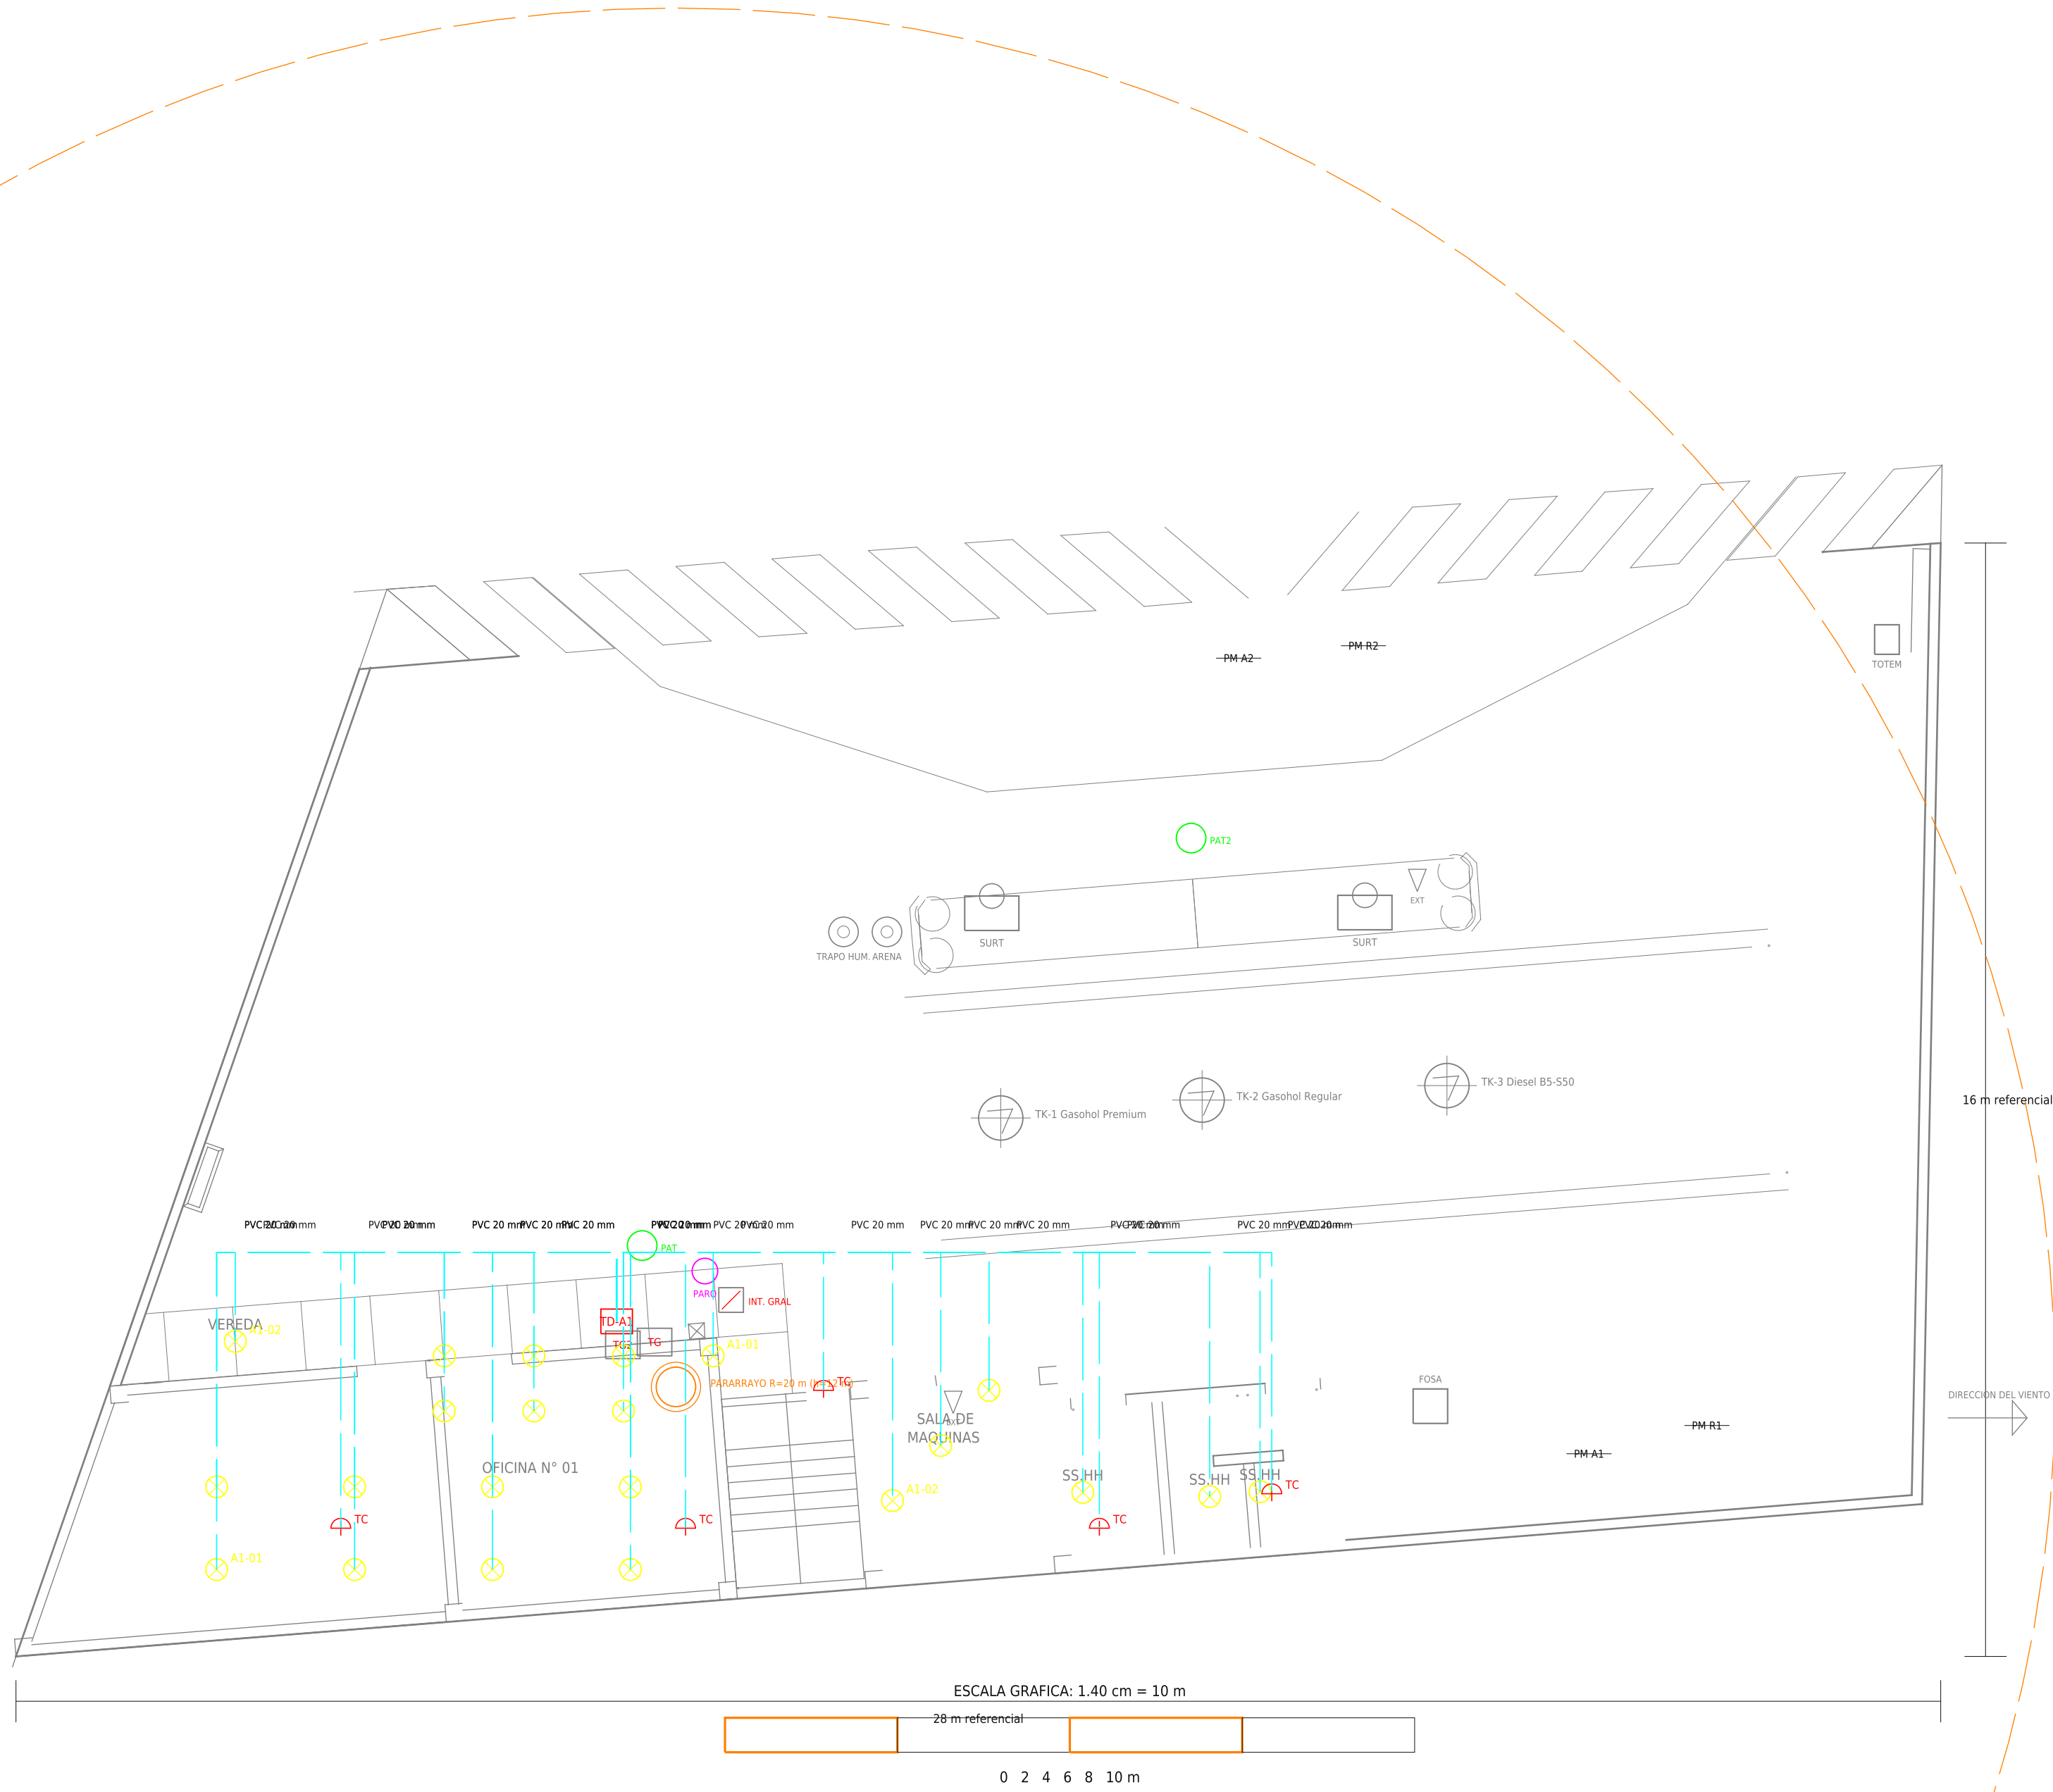

IE-02 LEYENDA	
	Luminaria LED interior (A1-01: admin./oficina; A1-02: SS.HH y sala de maquinas)
	Tomacorriente doble (TC), con contacto a tierra
	Tablero de distribucion TD-A1
	Canalizacion empotrada proyectada
	Tomacorrientes con interruptor diferencial 30 mA
CNE: conductor minimo 2.5 mm2; dV ramal <= 2.5 %	

NOTAS TECNICAS
Alumbrado interior con paneles LED 36 W y luminarias estancas 18 W. Tomas de corriente con puesta a tierra; circuito independiente por zona. Tuberia empotrada en muros y losa; cajas octogonales y rectangulares. Interruptores de pared a 1.20 m; tomacorrientes a 0.40 m del piso. Tablero TD-A1 alimentado desde TG (ver IE-05).



UNIVERSIDAD NACIONAL DEL ALTIPLANO				
FACULTAD DE INGENIERIA MECANICA ELECTRICA, ELECTRONICA Y SISTEMAS				
ESCUELA PROFESIONAL DE INGENIERIA MECANICA ELECTRICA				
PROYECTO: INSTALACIONES ELECTRICAS EN BAJA TENSION				
ESTACION DE SERVICIO (GRIFO) DE COMBUSTIBLES LIQUIDOS - ANTEPROYECTO NUEVO				
DIESEL B5-S50 / GASOHOL REGULAR / GASOHOL PREMIUM - SIN GLP NI GNV				
ALUMBRADO Y TOMACORRIENTES - EDIFICIO ADMINISTRATIVO				
PROPIETARIO: MIGUEL MAMANI CHUQUICALLATA				
DISTRITO: PROV.: SAN ROMAN - DEP.: PUNO				
UBICACION: PREDIO RUSTICO REUMITA PARCELA B-8 Y B-9, CARRETERA JULIACA-PUNO				
CURSO: INSTALACIONES ELECTRICAS I			DISENADO Y DIBUJADO: RENZO GABRIEL MAMANI GALINDO	
DOCENTE: MG. GREGORIO MEZA MAROCHO			REVISION DOCENTE: CAMPO ACADEMICO - SIN FIRMA NI APROBACION AFIRMADA	
MODALIDAD: INDIVIDUAL			SEMESTRE: 2026-II	
CODIGO EST.: 228447			SEDE: PUNO - PERU	
LAMINA IE-02	ESCALA 1:100 / IND.	FECHA AGOSTO 2026	REV. R00	HOJA 02/06
UNAP - PUNO ANTEPROYECTO SUJETO A VERIFICACION DE CAMPO, FACTIBILIDAD Y REVISION PROFESIONAL		NO SE CONSIGNA CIP, SELLO NI FIRMA POR NO EXISTIR ESOS DATOS EN LAS FUENTES		