


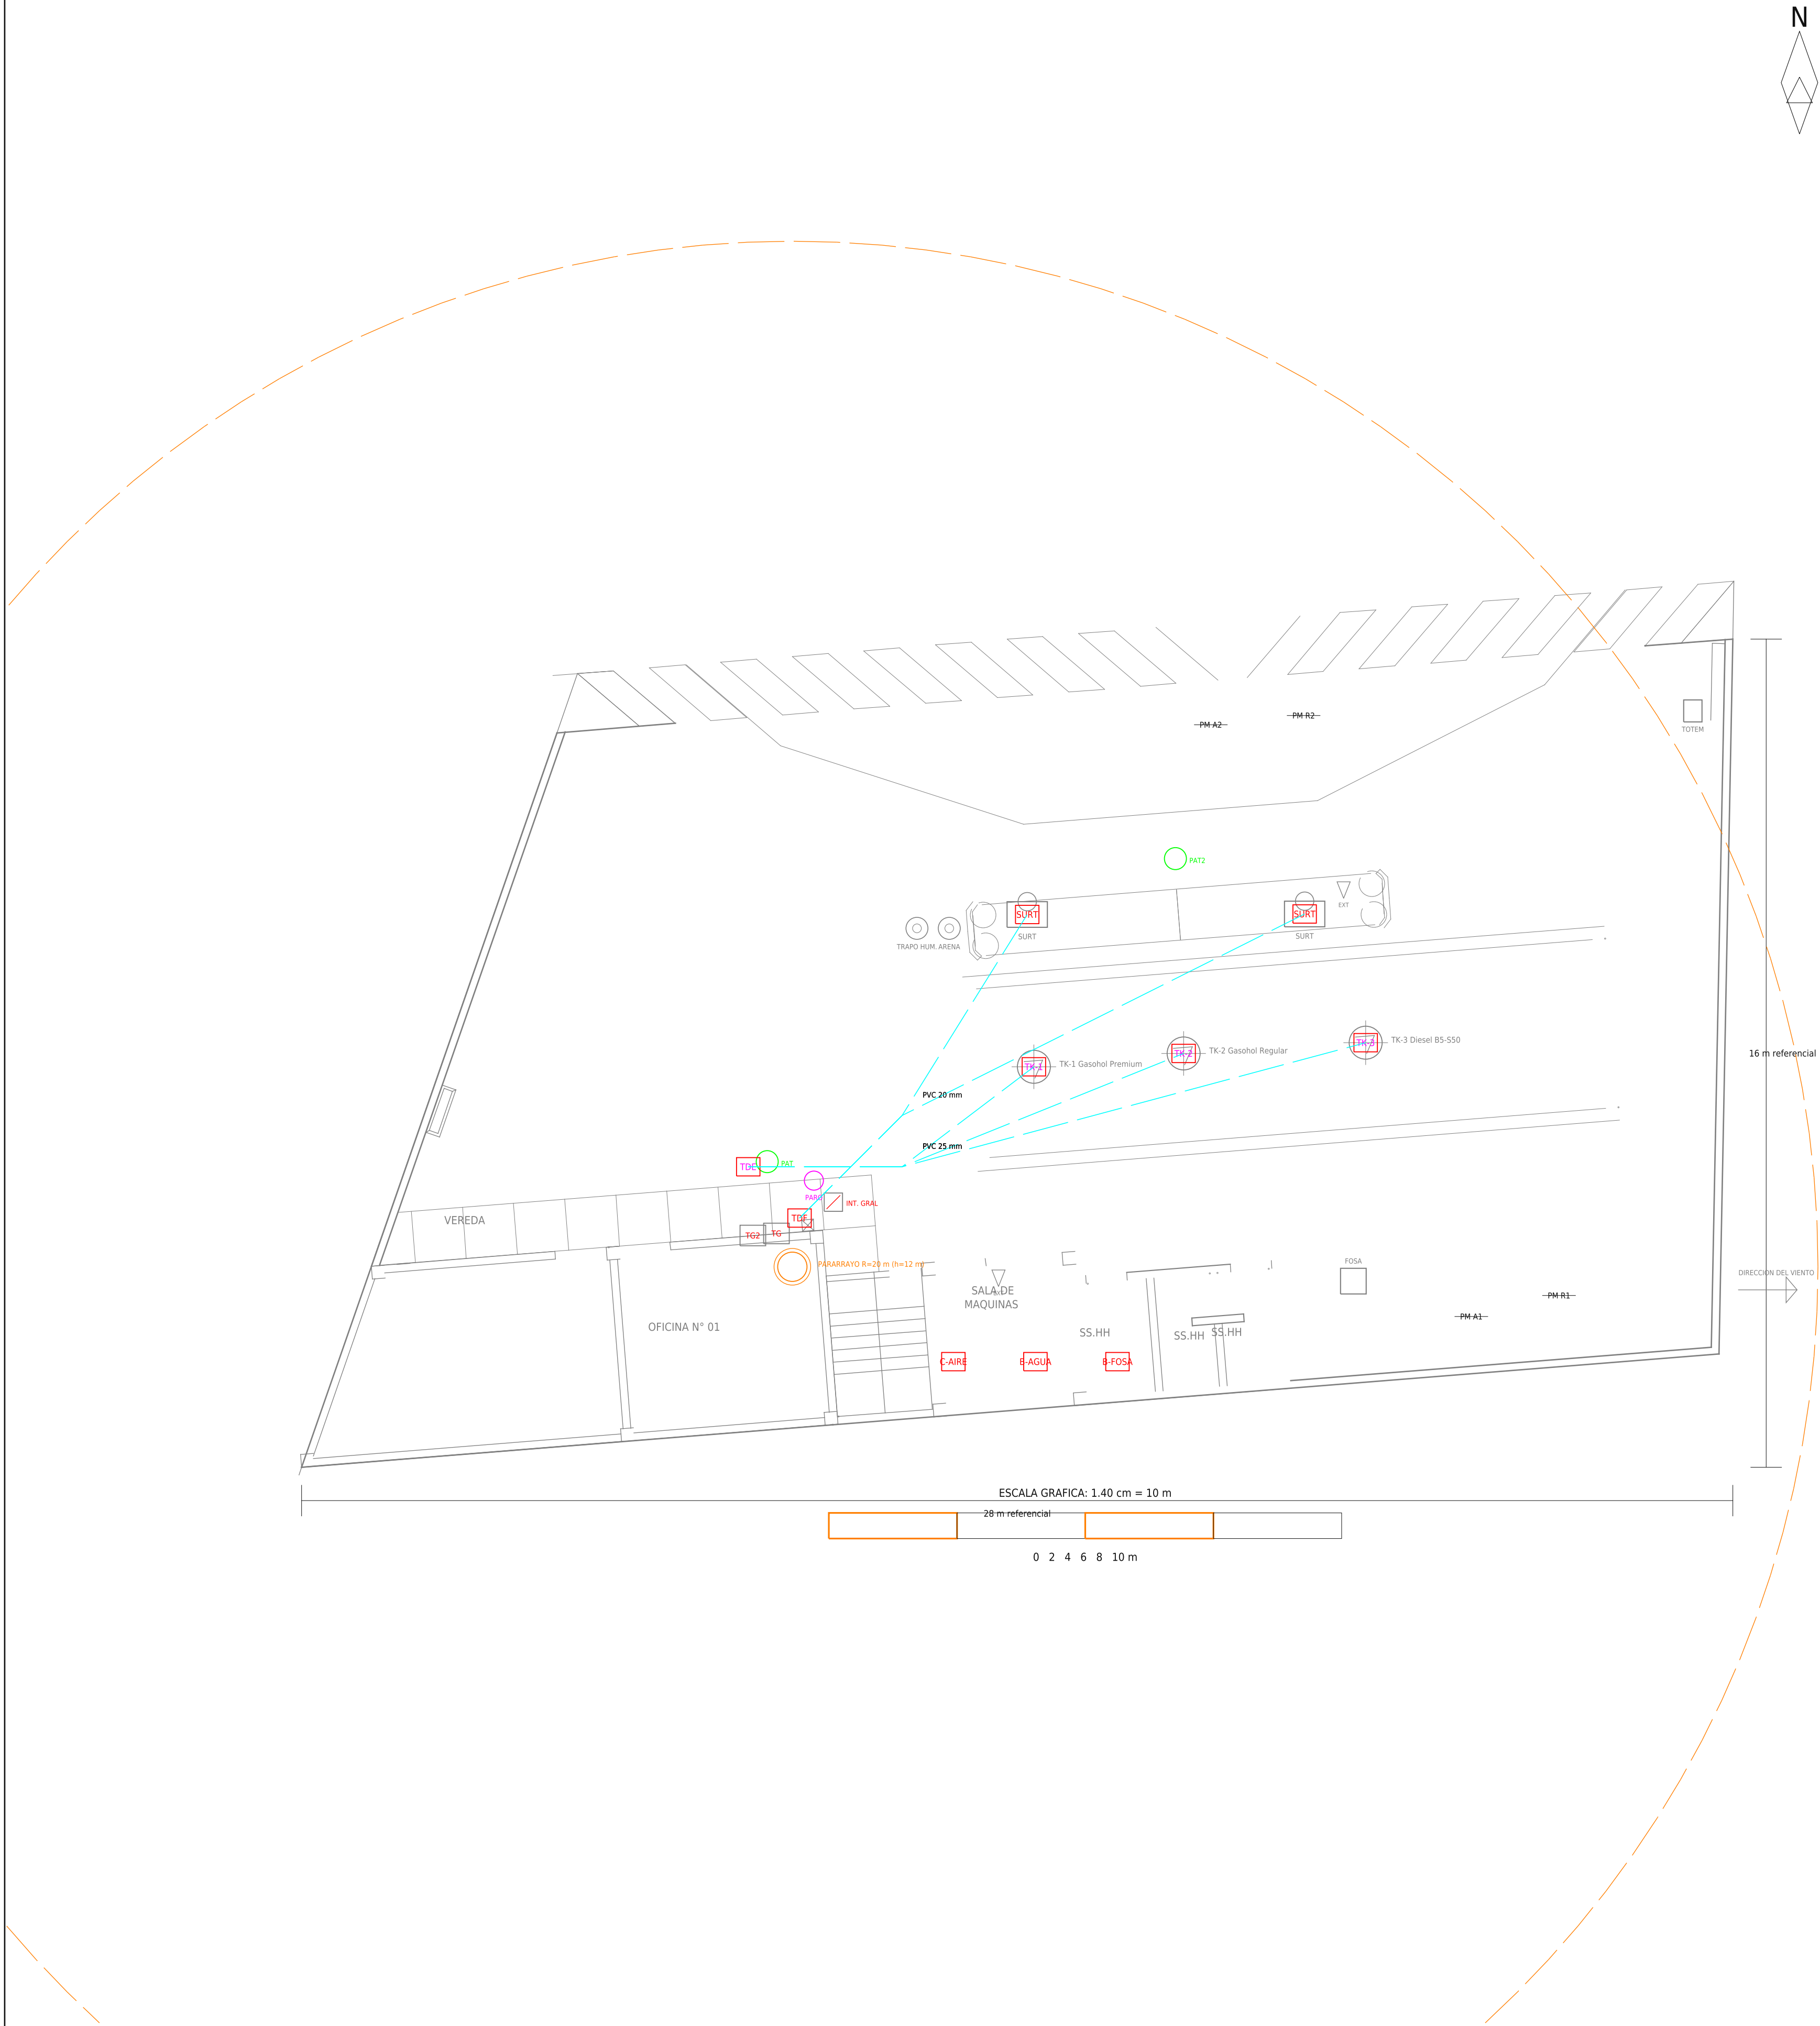

IE-03 LEYENDA	
	STP - bomba sumergible de tanque (emergencia, TDE)
	Surtidor / cabeza electronica (UPS-FUEL)
	Tablero de distribucion TDE (emergencia) / TDF (fuerza)
	Cana1izacion subterranea proyectada
	Pulsador de paro de emergencia de playa (S-04)
	C-AIRE = compresor de aire (F-07); B-AGUA = bomba de agua (F-08); B-FOSA = bomba de efluentes (F-09)
	Cargas criticas (STP, surtidores, ATG, POS) con respaldo de emergencia
	CNE: areas clasificadas con equipo de proteccion apropiada

NOTAS TECNICAS
STP de 1.5 hp con arranque directo; circuito de emergencia desde TDE. Surtidores con cabeza electronica 103 VA (UPS-FUEL 1.5 kVA). Pulsador de paro de emergencia de playa (S-04) accesible en cada isla. Equipos de servicio (compresor, bombas) en sala de maquinas desde TDF. Cana1izaciones a tanques y surtidores en zanja a 0.60 m.

UNIVERSIDAD NACIONAL DEL ALTIPLANO				
FACULTAD DE INGENIERIA MECANICA ELECTRICA, ELECTRONICA Y SISTEMAS				
ESCUELA PROFESIONAL DE INGENIERIA MECANICA ELECTRICA				
PROYECTO: INSTALACIONES ELECTRICAS EN BAJA TENSION				
ESTACION DE SERVICIO (GRIFO) DE COMBUSTIBLES LIQUIDOS - ANTEPROYECTO NUEVO				
DIESEL B5-S50 / GASOHOL REGULAR / GASOHOL PREMIUM - SIN GLP NI GNV				
FUERZA, SURTIDORES, BOMBAS Y PARO DE EMERGENCIA				
PROPIETARIO: MIGUEL MAMANI CHUQUICALLATA				
DISTRITO: PROV.: SAN ROMAN - DEP.: PUNO				
UBICACION: PREDIO RUSTICO REUMITA PARCELA B-8 Y B-9, CARRETERA JULIACA-PUNO				
CURSO: INSTALACIONES ELECTRICAS I			DISENADO Y DIBUJADO: RENZO GABRIEL MAMANI GALINDO	
DOCENTE: MG. GREGORIO MEZA MAROCHO			REVISION DOCENTE: CAMPO ACADEMICO - SIN FIRMA NI APROBACION AFIRMADA	
MODALIDAD: INDIVIDUAL			SEMESTRE: 2026-II	
CODIGO EST.: 228447			SEDE: PUNO - PERU	
LAMINA IE-03	ESCALA 1:100 / IND.	FECHA AGOSTO 2026	REV. R00	HOJA 03/06
UNAP - PUNO ANTEPROYECTO SUJETO A VERIFICACION DE CAMPO, FACTIBILIDAD Y REVISION PROFESIONAL		NO SE CONSIGNA CIP, SELLO NI FIRMA POR NO EXISTIR ESOS DATOS EN LAS FUENTES		