


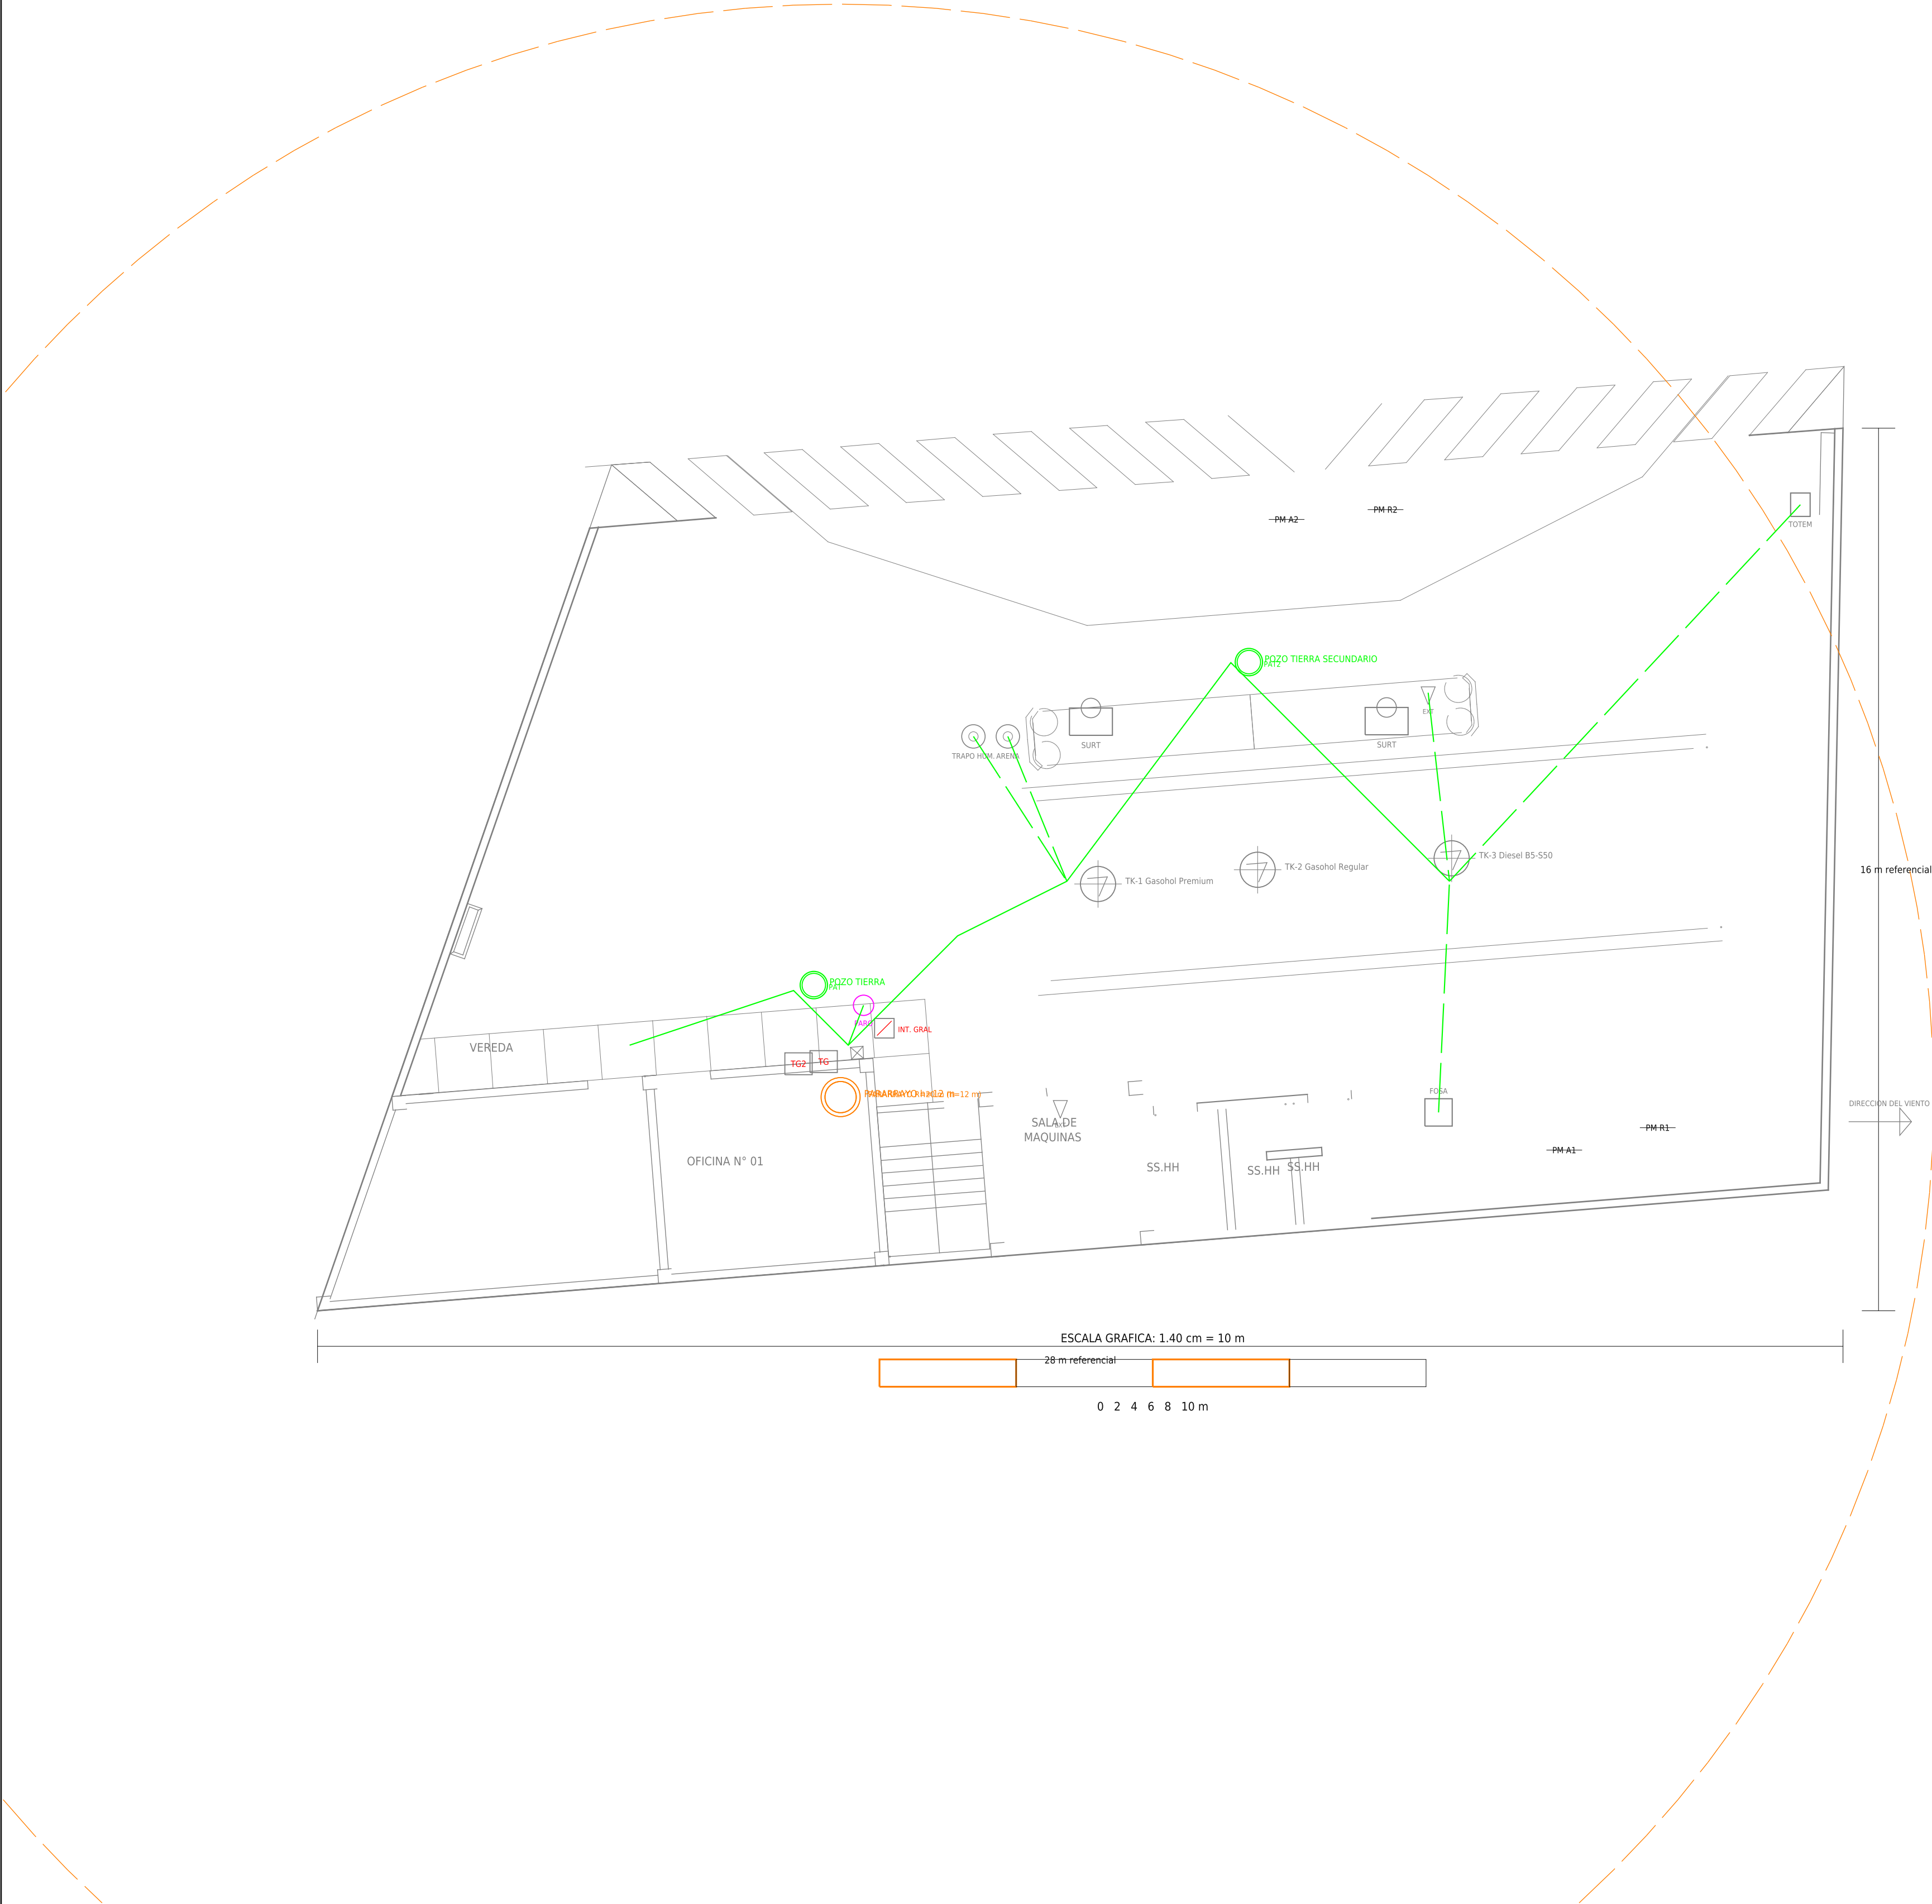

NOTAS TECNICAS	
PAT principal junto al TG: 2 pozos (PAT/PAT2) con varilla Cu 5/8 x 2.4 m.	
Enlace equipotencial de tableros, surtidores, tanques y fosa a la malla.	
Pararrayo h=12 m con radio de proteccion 20 m (electrogeometrico).	
Conductor de tierra desnudo Cu 10 mm2 enterrado a 0.50 m.	
Verificar resistencia con telurometro en campo.	

UNIVERSIDAD NACIONAL DEL ALTIPLANO					
FACULTAD DE INGENIERIA MECANICA ELECTRICA, ELECTRONICA Y SISTEMAS					
ESCUELA PROFESIONAL DE INGENIERIA MECANICA ELECTRICA					
PROYECTO: INSTALACIONES ELECTRICAS EN BAJA TENSION					
ESTACION DE SERVICIO (GRIFO) DE COMBUSTIBLES LIQUIDOS - ANTEPROYECTO NUEVO					
DIESEL B5-S50 / GASOHOL REGULAR / GASOHOL PREMIUM - SIN GLP NI GNV					
PUESTA A TIERRA, EQUIPOTENCIALIDAD Y PROTECCION CONTRA EL RAYO					
PROPIETARIO: MIGUEL MAMANI CHUQUICALLATA					
DISTRITO/PROV.: SAN ROMAN - DEP.: PUNO					
UBICACION: PREDIO RUSTICO REUMITA PARCELA B-8 Y B-9, CARRETERA JULIACA-PUNO					
CURSO: INSTALACIONES ELECTRICAS I			DISENADO Y DIBUJADO: RENZO GABRIEL MAMANI GALINDO		
DOCENTE: MG. GREGORIO MEZA MAROCHO			REVISION DOCENTE: CAMPO ACADEMICO - SIN FIRMA NI APROBACION AFIRMADA		
MODALIDAD: INDIVIDUAL			SEMESTRE: 2026-II		
CODIGO EST.: 228447			SEDE: PUNO - PERU		
LAMINA	ESCALA		FECHA	REV.	HOJA
IE-04	1:100 / IND.		AGOSTO 2026	R00	04/06
UNAP - PUNO ANTEPROYECTO SUJETO A VERIFICACION DE CAMPO, FACTIBILIDAD Y REVISION PROFESIONAL			NO SE CONSIGNA CIP, SELLO NI FIRMA POR NO EXISTIR ESOS DATOS EN LAS FUENTES		