


DIAGRAMA UNIFILAR GENERAL 380/220 V - 3F+N+PE - GRIFO SAN ROMÁN

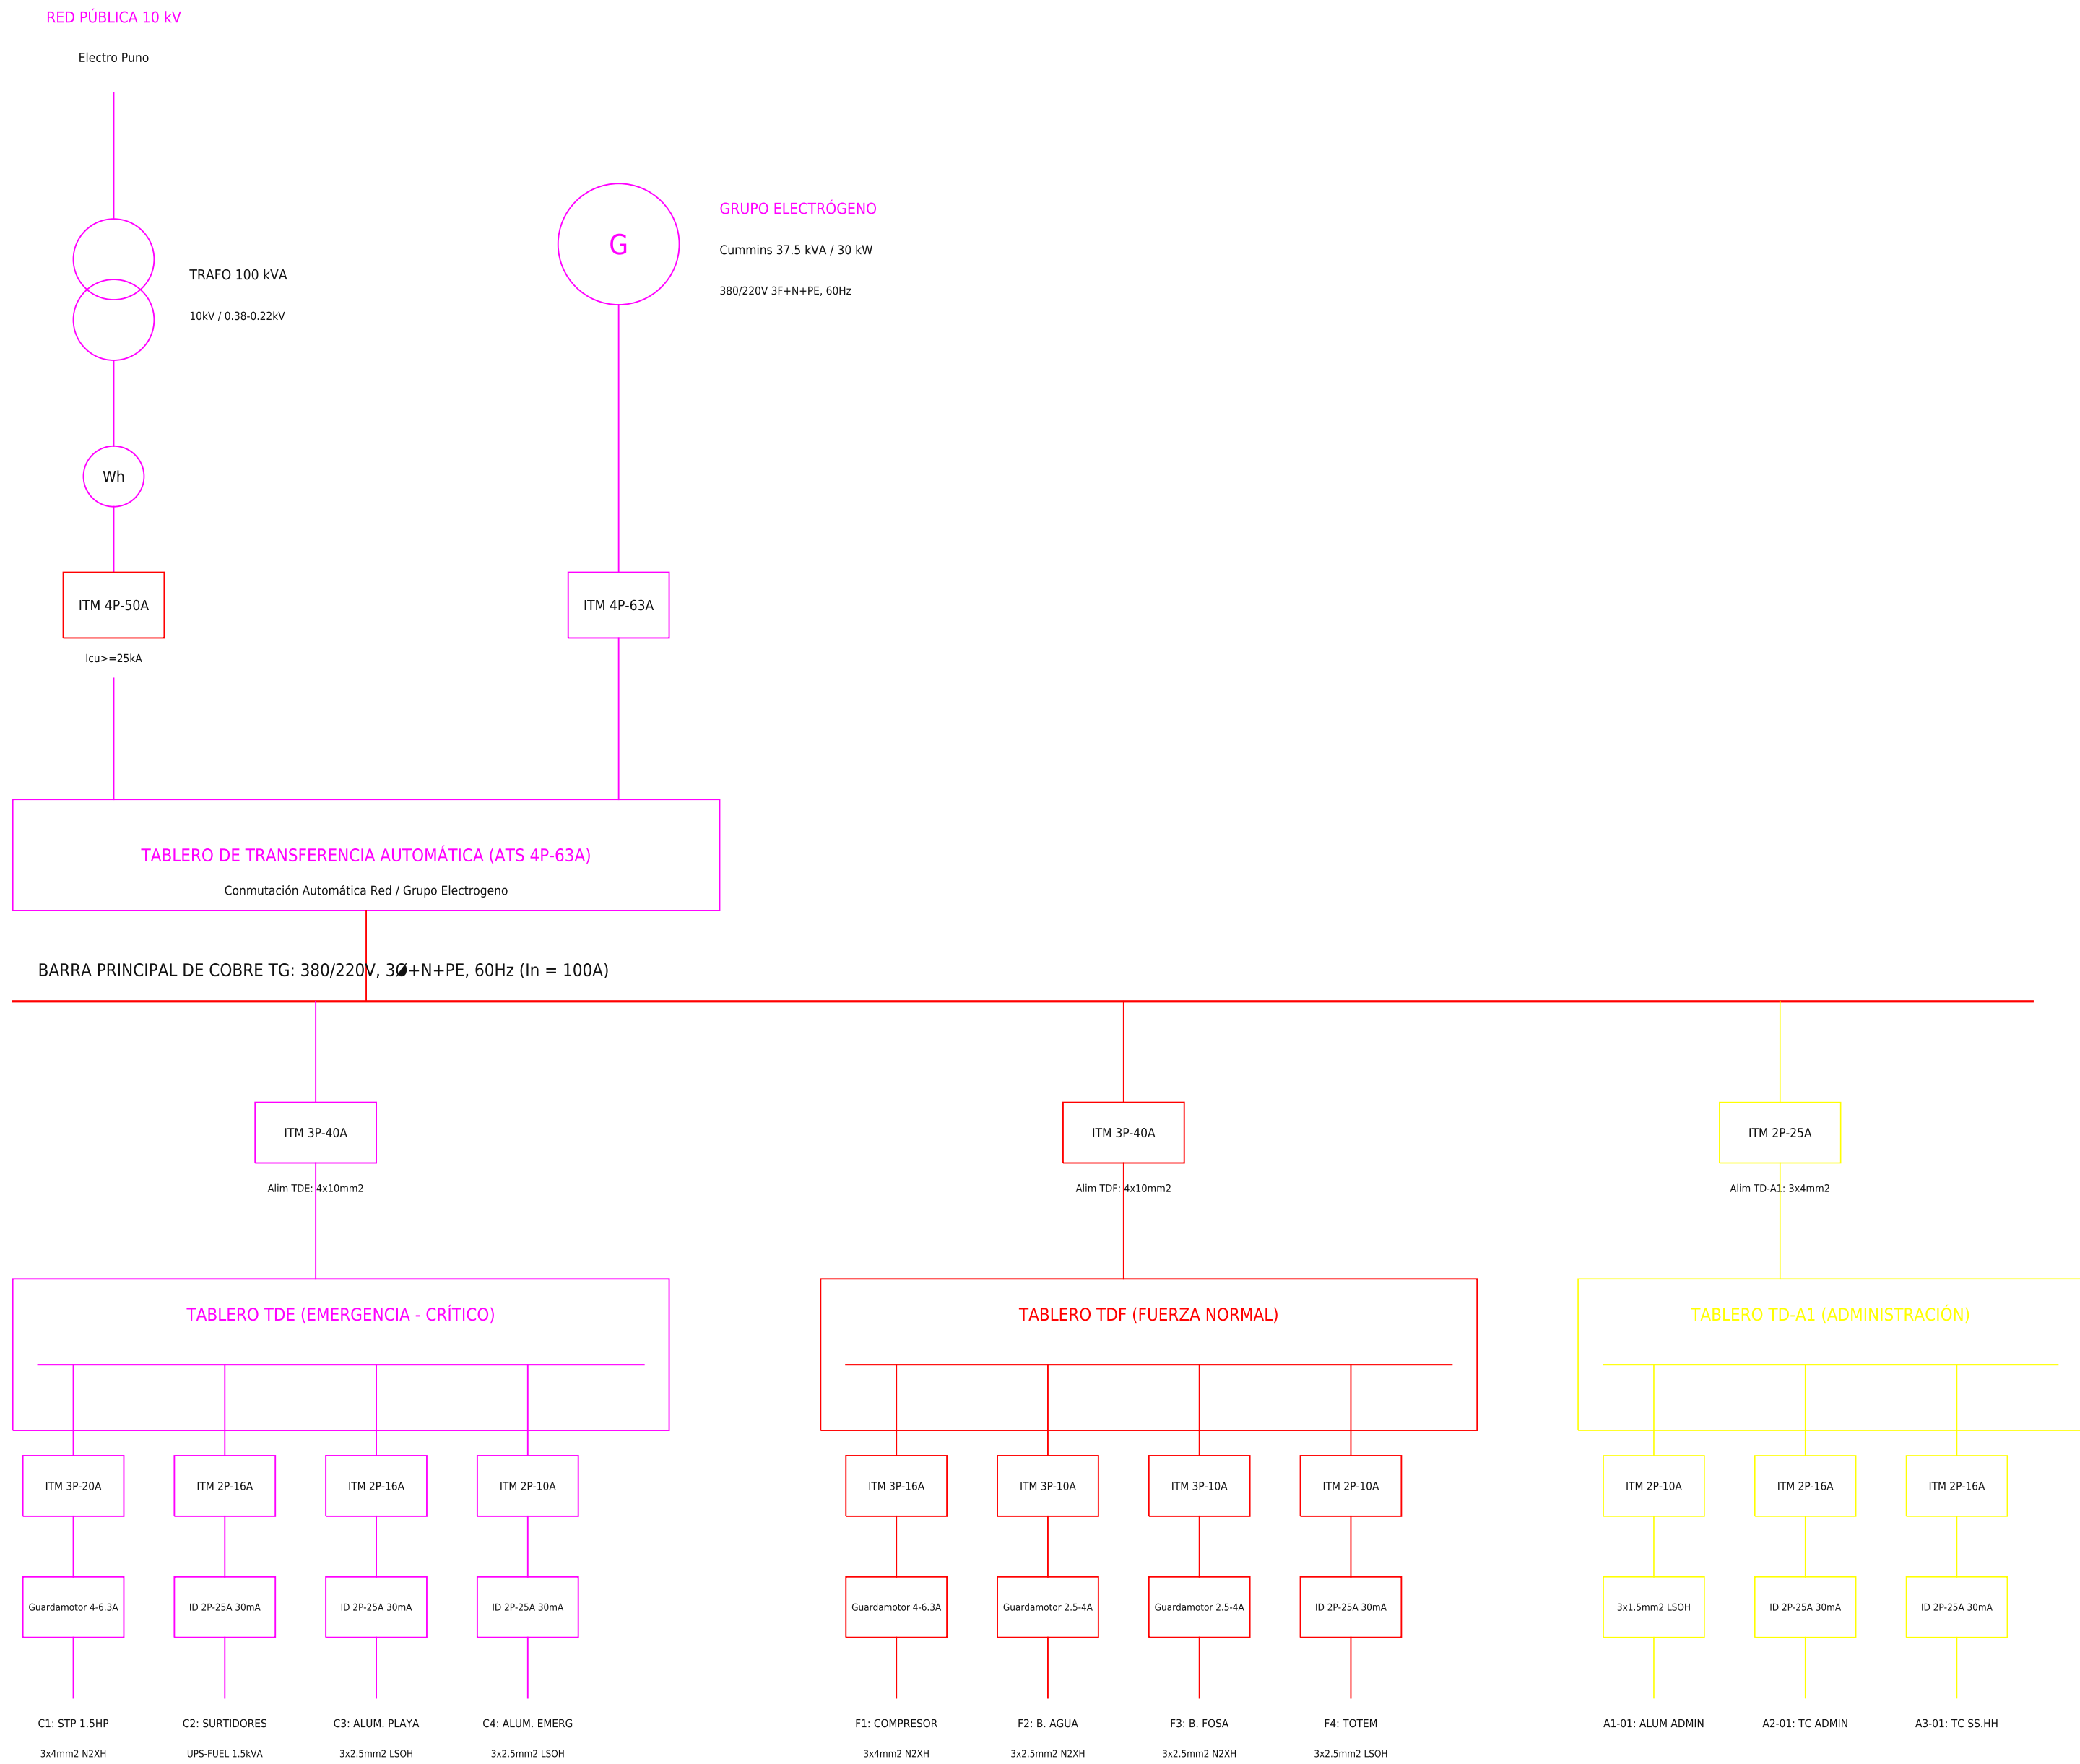

CUADRO RESUMIDO DE CARGAS (CNE-U)							
ID	TAB	FASE	kVA	ITM	Cu/PE	dV	
F-01	TDE	R	2.42	20 A	4/4	1.35%	
F-02	TDE	S	2.42	20 A	4/4	1.43%	
F-03	TDE	T	2.42	20 A	4/4	1.55%	
F-04	UPS-FUEL	R	0.10	16 A	2.5/2.5	0.43%	
F-05	UPS-FUEL	S	0.10	16 A	2.5/2.5	0.45%	
F-06	UPS-FUEL	T	0.40	10 A	2.5/2.5	0.54%	
F-07	TDF	RST	2.75	16 A	4/4	0.44%	
F-08	TDF	RST	1.88	10 A	4/4	0.43%	
F-09	TDF	RST	1.88	10 A	4/4	0.49%	
L-01	TDE	R	0.84	10 A	2.5/2.5	1.18%	
L-02	TDF	S	0.67	10 A	2.5/2.5	1.19%	
L-03	TDF	T	0.42	10 A	2.5/2.5	0.71%	
A1-01	TD-A1	R	0.57	10 A	2.5/2.5	0.79%	
A1-02	TD-A1	S	0.23	10 A	2.5/2.5	0.55%	
A1-03	TD-A1	R	1.20	20 A	4/4	0.93%	
A1-04	TD-A1	T	1.00	20 A	4/4	0.81%	
A1-05	TDE	T	0.80	16 A	2.5/2.5	0.73%	
S-01	UPS-IT	S	1.20	10 A	2.5/2.5	1.29%	
S-02	TDE	T	0.20	10 A	2.5/2.5	0.47%	
S-03	TDE	R	0.30	10 A	2.5/2.5	0.63%	
S-04	TDE	S	0.10	10 A	2.5/2.5	0.43%	
S-05	TDE	S	0.15	10 A	2.5/2.5	0.49%	

PARÁMETROS GENERALES DEL ANTEPROYECTO - GRIFO SAN ROMÁN

- Potencia Instalada Total (PI): 18.25 kW (22.05 kVA)
- Máxima Demanda Estimada (MD): 15.08 kW (18.20 kVA)
- Capacidad del Servicio Sugerida: 30 kVA (Reserva CNE = 21.84 kVA)
- Corriente Máxima de Diseño: 33.4 A | Interruptor General: 4P-50A
- Caída de Tensión Alimentador Principal: 0.22% (CNE máximo permitido = 2.5%)

UNIVERSIDAD NACIONAL DEL ALTIPLANO

FACULTAD DE INGENIERIA MECANICA ELECTRICA, ELECTRONICA Y SISTEMAS

ESCUELA PROFESIONAL DE INGENIERIA MECANICA ELECTRICA

PROYECTO: INSTALACIONES ELECTRICAS EN BAJA TENSION

ESTACION DE SERVICIO (GRIFO) DE COMBUSTIBLES LIQUIDOS - ANTEPROYECTO NUEVO

DIESEL B5-S50 / GASOHOL REGULAR / GASOHOL PREMIUM - SIN GLP NI GNV

DIAGRAMA UNIFILAR, CUADROS DE CARGA Y TABLEROS

PROPIETARIO: MIGUEL MAMANI CHUQUICALLATA

DISTRITO: PROV.: SAN ROMAN - DEP.: PUNO

UBICACION: PREDIO RUSTICO REUMITA PARCELA B-8 Y B-9, CARRETERA JULIACA-PUNO

CURSO: INSTALACIONES ELECTRICAS I
DOCENTE: MG. GREGORIO MEZA MAROCHO

DISENADO Y DIBUJADO: RENZO GABRIEL MAMANI GALINDO

REVISION DOCENTE: CAMPO ACADEMICO - SIN FIRMA NI APROBACION AFIRMADA

MODALIDAD: INDIVIDUAL

CODIGO EST.: 228447

SEMESTRE: 2026-II

SEDE: PUNO - PERU

LAMINA

IE-05

ESCALA

S/E

FECHA

AGOSTO 2026

REV.

R00

HOJA

05/06

UNAP - PUNO | ANTEPROYECTO SUJETO A VERIFICACION DE CAMPO, FACTIBILIDAD Y REVISION PROFESIONAL
NO SE CONSIGNA CIP, SELLO NI FIRMA POR NO EXISTIR ESOS DATOS EN LAS FUENTES