


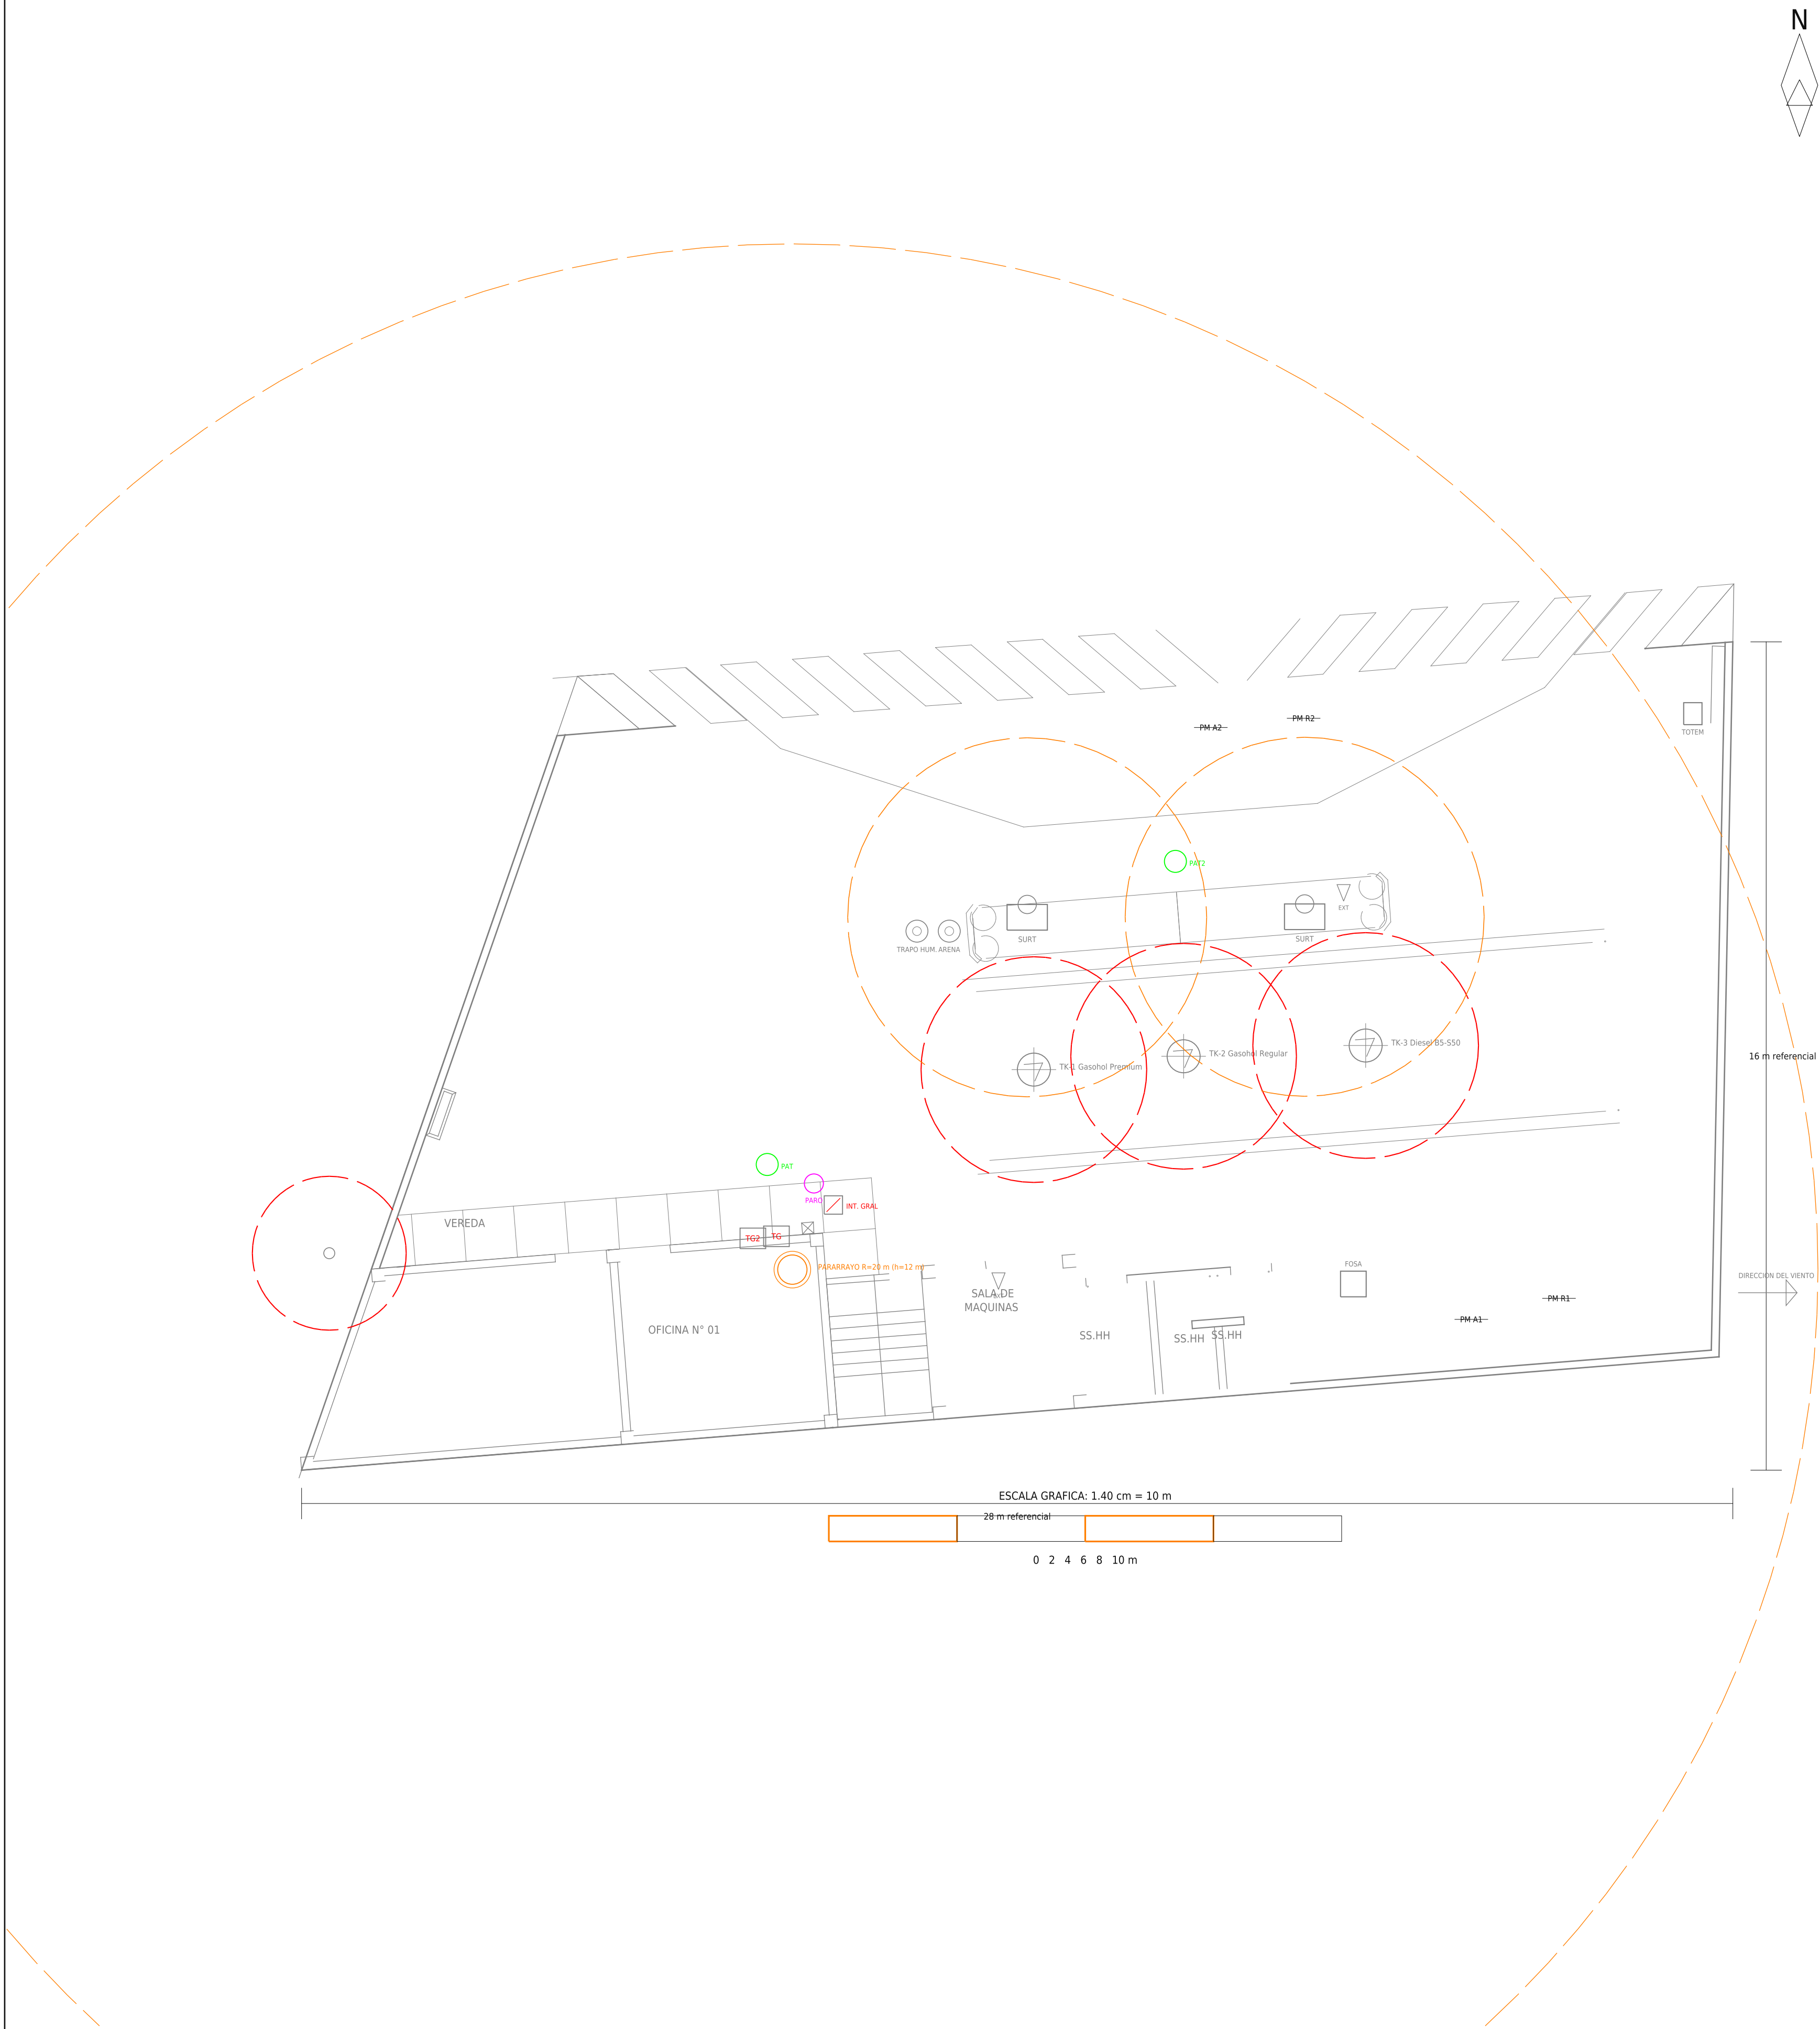

IE-06 CLASIFICACION DE AREAS	
	Zona 1 - area peligrosa alrededor de tanques y venteos
	Zona 2 - area de despacho alrededor de surtidores
	Tanque subteraneo TK (punto de riesgo)
	Surtidor de despacho
	Direccion del viento (referencia para dispersion de vapores)
Lmites: propuesta academica; trazado segun CNE-U cap. 6 y revision competente	
CNE: equipo electrico de areas clasificadas con proteccion apropiada	

NOTAS TECNICAS
Zona 1 (r=2.2 m) alrededor de tanques y venteos; Zona 2 (r=3.5 m) en despacho. Venteo de tanques con zona 1 (r=1.5 m) adicional. Equipo electrico en Zona 1/2: certificado para clasificacion de gases (E, ex d / ex c). Surtidores con cabeza electronica intrinsecamente segura. Clasificacion preliminar: sujeto a revision competente y normativa sectorial.

UNIVERSIDAD NACIONAL DEL ALTIPLANO				
FACULTAD DE INGENIERIA MECANICA ELECTRICA, ELECTRONICA Y SISTEMAS				
ESCUELA PROFESIONAL DE INGENIERIA MECANICA ELECTRICA				
PROYECTO: INSTALACIONES ELECTRICAS EN BAJA TENSION				
ESTACION DE SERVICIO (GRIFO) DE COMBUSTIBLES LIQUIDOS - ANTEPROYECTO NUEVO				
DIESEL B5-S50 / GASOHOL REGULAR / GASOHOL PREMIUM - SIN GLP NI GNV				
CLASIFICACION DE AREAS PELIGROSAS Y DETALLES				
PROPIETARIO: MIGUEL MAMANI CHUQUICALLATA				
DISTRITO: PROV.: SAN ROMAN - DEP.: PUNO				
UBICACION: PREDIO RUSTICO REUMITA PARCELA B-8 Y B-9, CARRETERA JULIACA-PUNO				
CURSO: INSTALACIONES ELECTRICAS I			DISENADO Y DIBUJADO: RENZO GABRIEL MAMANI GALINDO	
DOCENTE: MG. GREGORIO MEZA MAROCHO			REVISION DOCENTE: CAMPO ACADEMICO - SIN FIRMA NI APROBACION AFIRMADA	
MODALIDAD: INDIVIDUAL			SEMESTRE: 2026-II	
CODIGO EST.: 228447			SEDE: PUNO - PERU	
LAMINA IE-06	ESCALA 1:100 / IND.	FECHA AGOSTO 2026	REV. R00	HOJA 06/06
UNAP - PUNO ANTEPROYECTO SUJETO A VERIFICACION DE CAMPO, FACTIBILIDAD Y REVISION PROFESIONAL				
NO SE CONSIGNA CIP, SELLO NI FIRMA POR NO EXISTIR ESOS DATOS EN LAS FUENTES				