PLANO ELECTRICO - PISO 1 V4

Casa de Aquiles - primer nivel

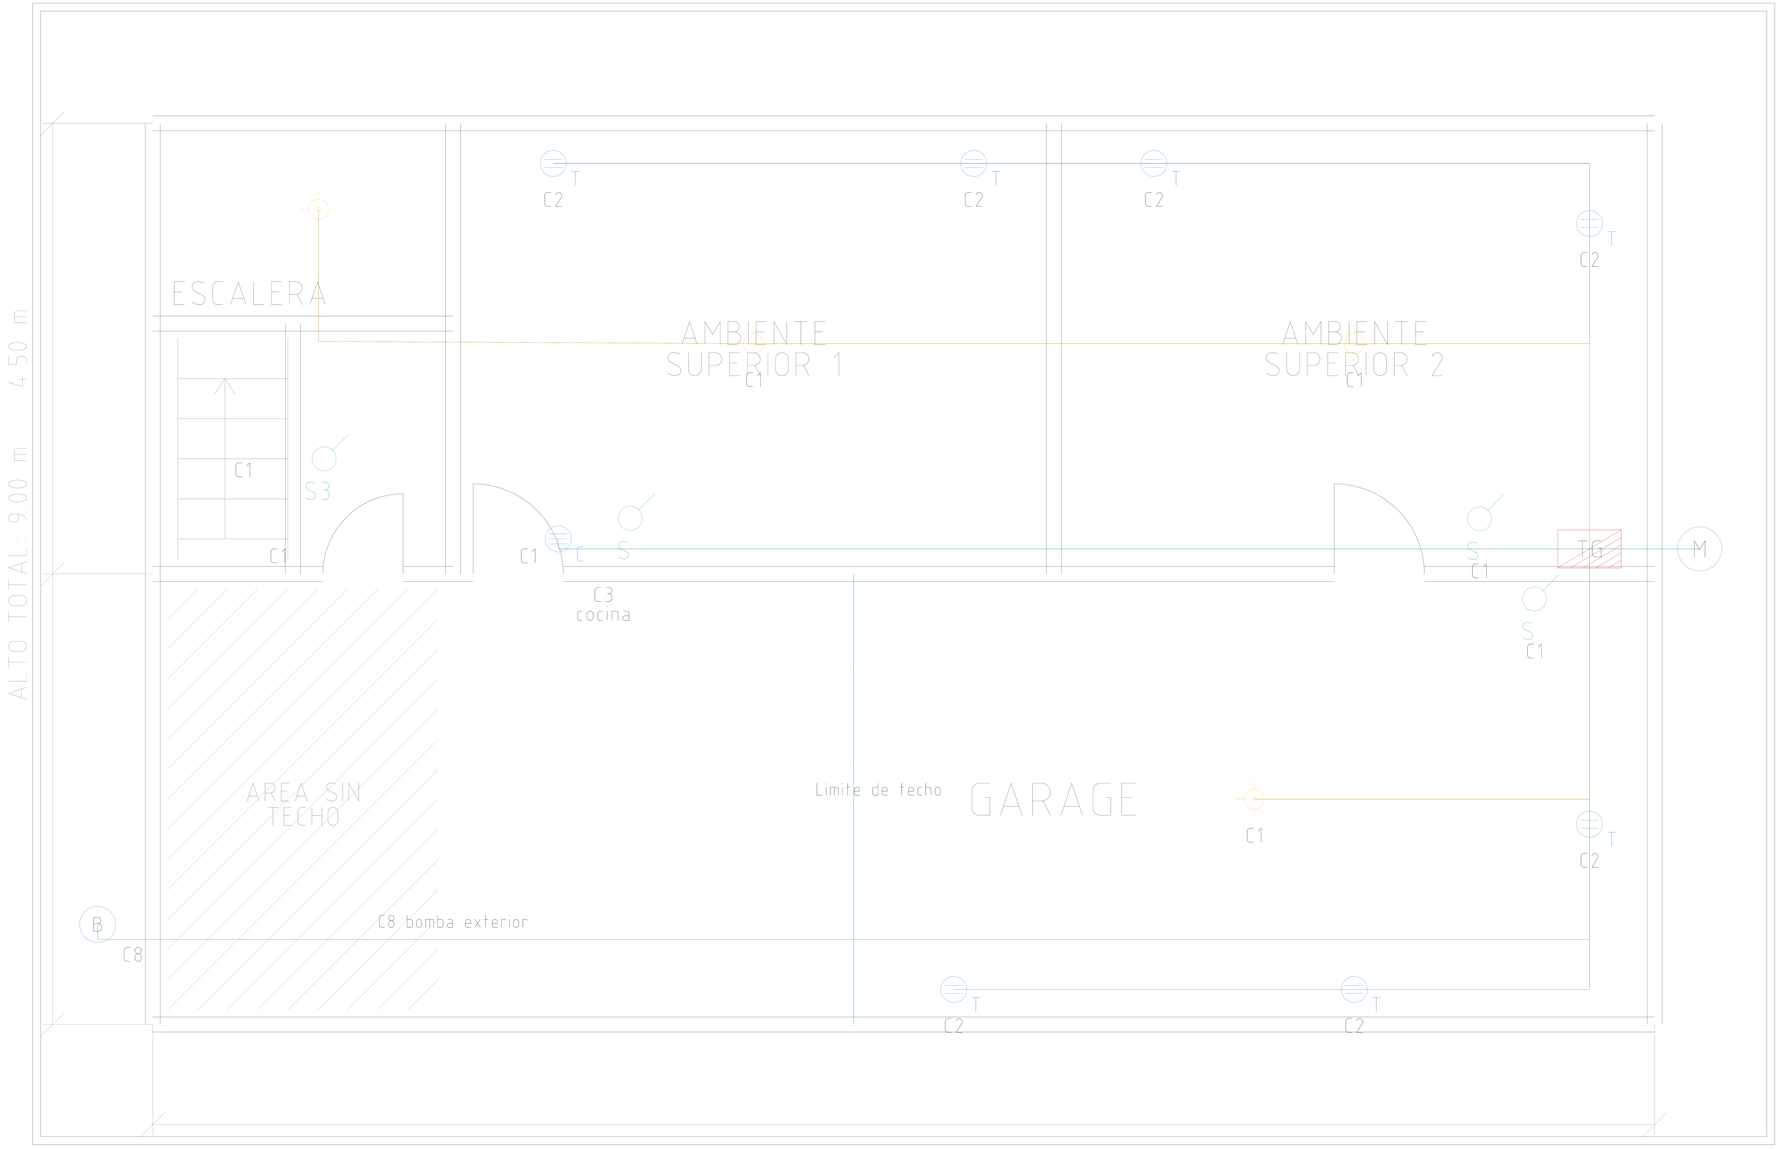

LEYENDA ELECTRICA

Simbolos:

- Soquete para foco
- Interruptor simple
- Tomacorriente con tierra
- Toma especial cocina
- TG Tablero general TG
- M Medidor M
- B Bomba exterior

Lineas:

- C1 Alumbrado
- C2 Tomacorrientes
- C3 Cocina
- C8 Bomba exterior
- Alimentador M-TG
- Limite de techo

Lineas discontinuas: canalizacion empotrada